


TECHNISCHE ZEICHNUNG - ALUMINIUMBLECH t = 1 mm

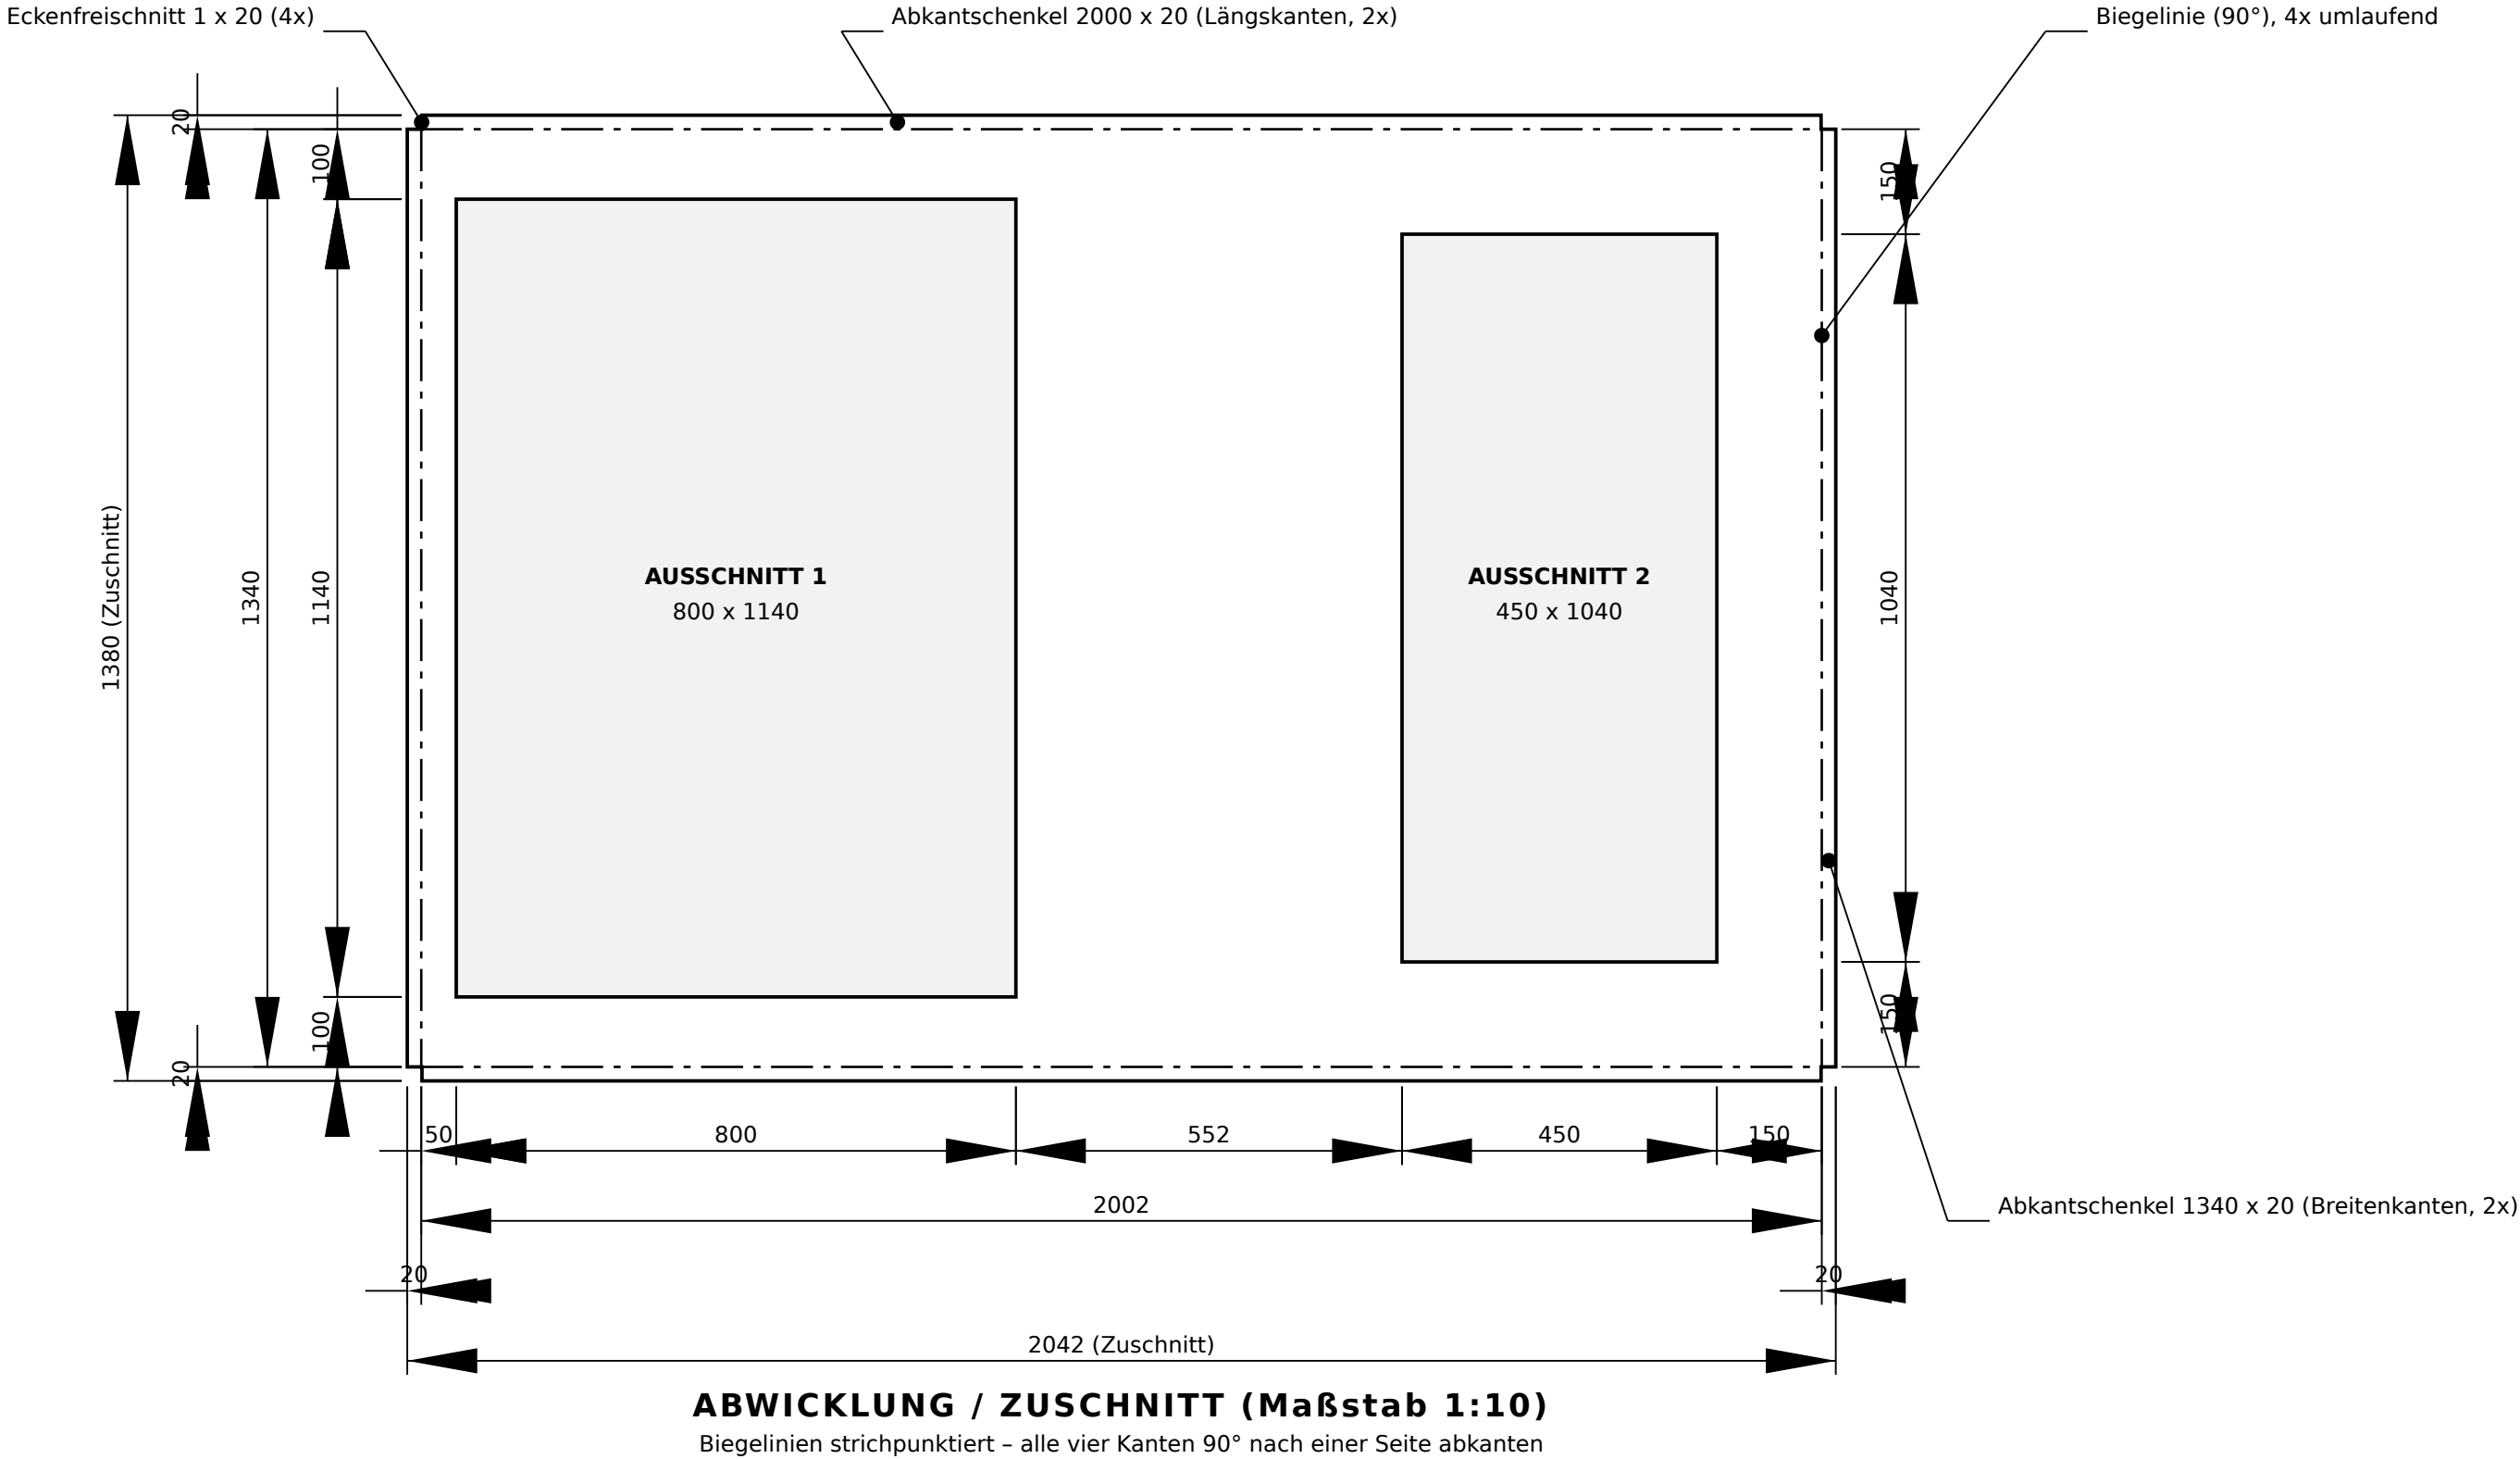


GEWICHTSBERECHNUNG (Aluminium, t = 1 mm, Flächengewicht 2,75 kg/m²)

Pos.	Beschreibung	Rechnung	Fläche [m²]	Gewicht [kg]
1	Grundfläche	2,002 m x 1,340 m	2,682680	7,377370
2	Abkantung Längskanten (2x)	2 x 2,000 m x 0,020 m	0,080000	0,220000
3	Abkantung Breitenkanten (2x)	2 x 1,340 m x 0,020 m	0,053600	0,147400
4	Zuschnitt brutto (1+2+3)	-	2,816280	7,744770
5	Abzug Ausschnitt 1	0,800 m x 1,140 m	-0,912000	-2,508000
6	Abzug Ausschnitt 2	0,450 m x 1,040 m	-0,468000	-1,287000
7	NETTO (4-5-6)	Fläche x 2,75 kg/m²	1,436280	3,949770

Gesamtgewicht des fertigen Bauteils: m = 1,436280 m² x 2,75 kg/m² = 3,9498 kg ≈ 3,95 kg

Zuschnitt vor dem Ausschneiden: 7,74 kg | Butzen/Verschnitt der Ausschnitte: 3,80 kg

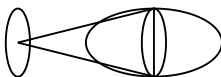

Projektionsmethode 1

Benennung Blechwanne, gekantet		Zeichnungs-Nr. TZ-AL-2002x1340-01	
Ausführung Abwicklung / Zuschnitt		Blatt 2 von 2	
Werkstoff Aluminium (Al), Blech EN AW / DIN EN 485		Blechdicke t = 1 mm	
Rohteil / Abwicklung 2042 x 1380 mm (2,81628 m²)		Flächengewicht 2,75 kg/m²	
Oberfläche / Kanten entgratet, scharfe Kanten gebrochen		Nettogewicht m = 3,95 kg	
Maßstab 1:10	Einheit mm	Projektion Methode 1 (E)	Allgemeintol. ISO 2768-mK
Datum 2026-09-05	Erstellt -	Geprüft -	Zust. / Änd. A